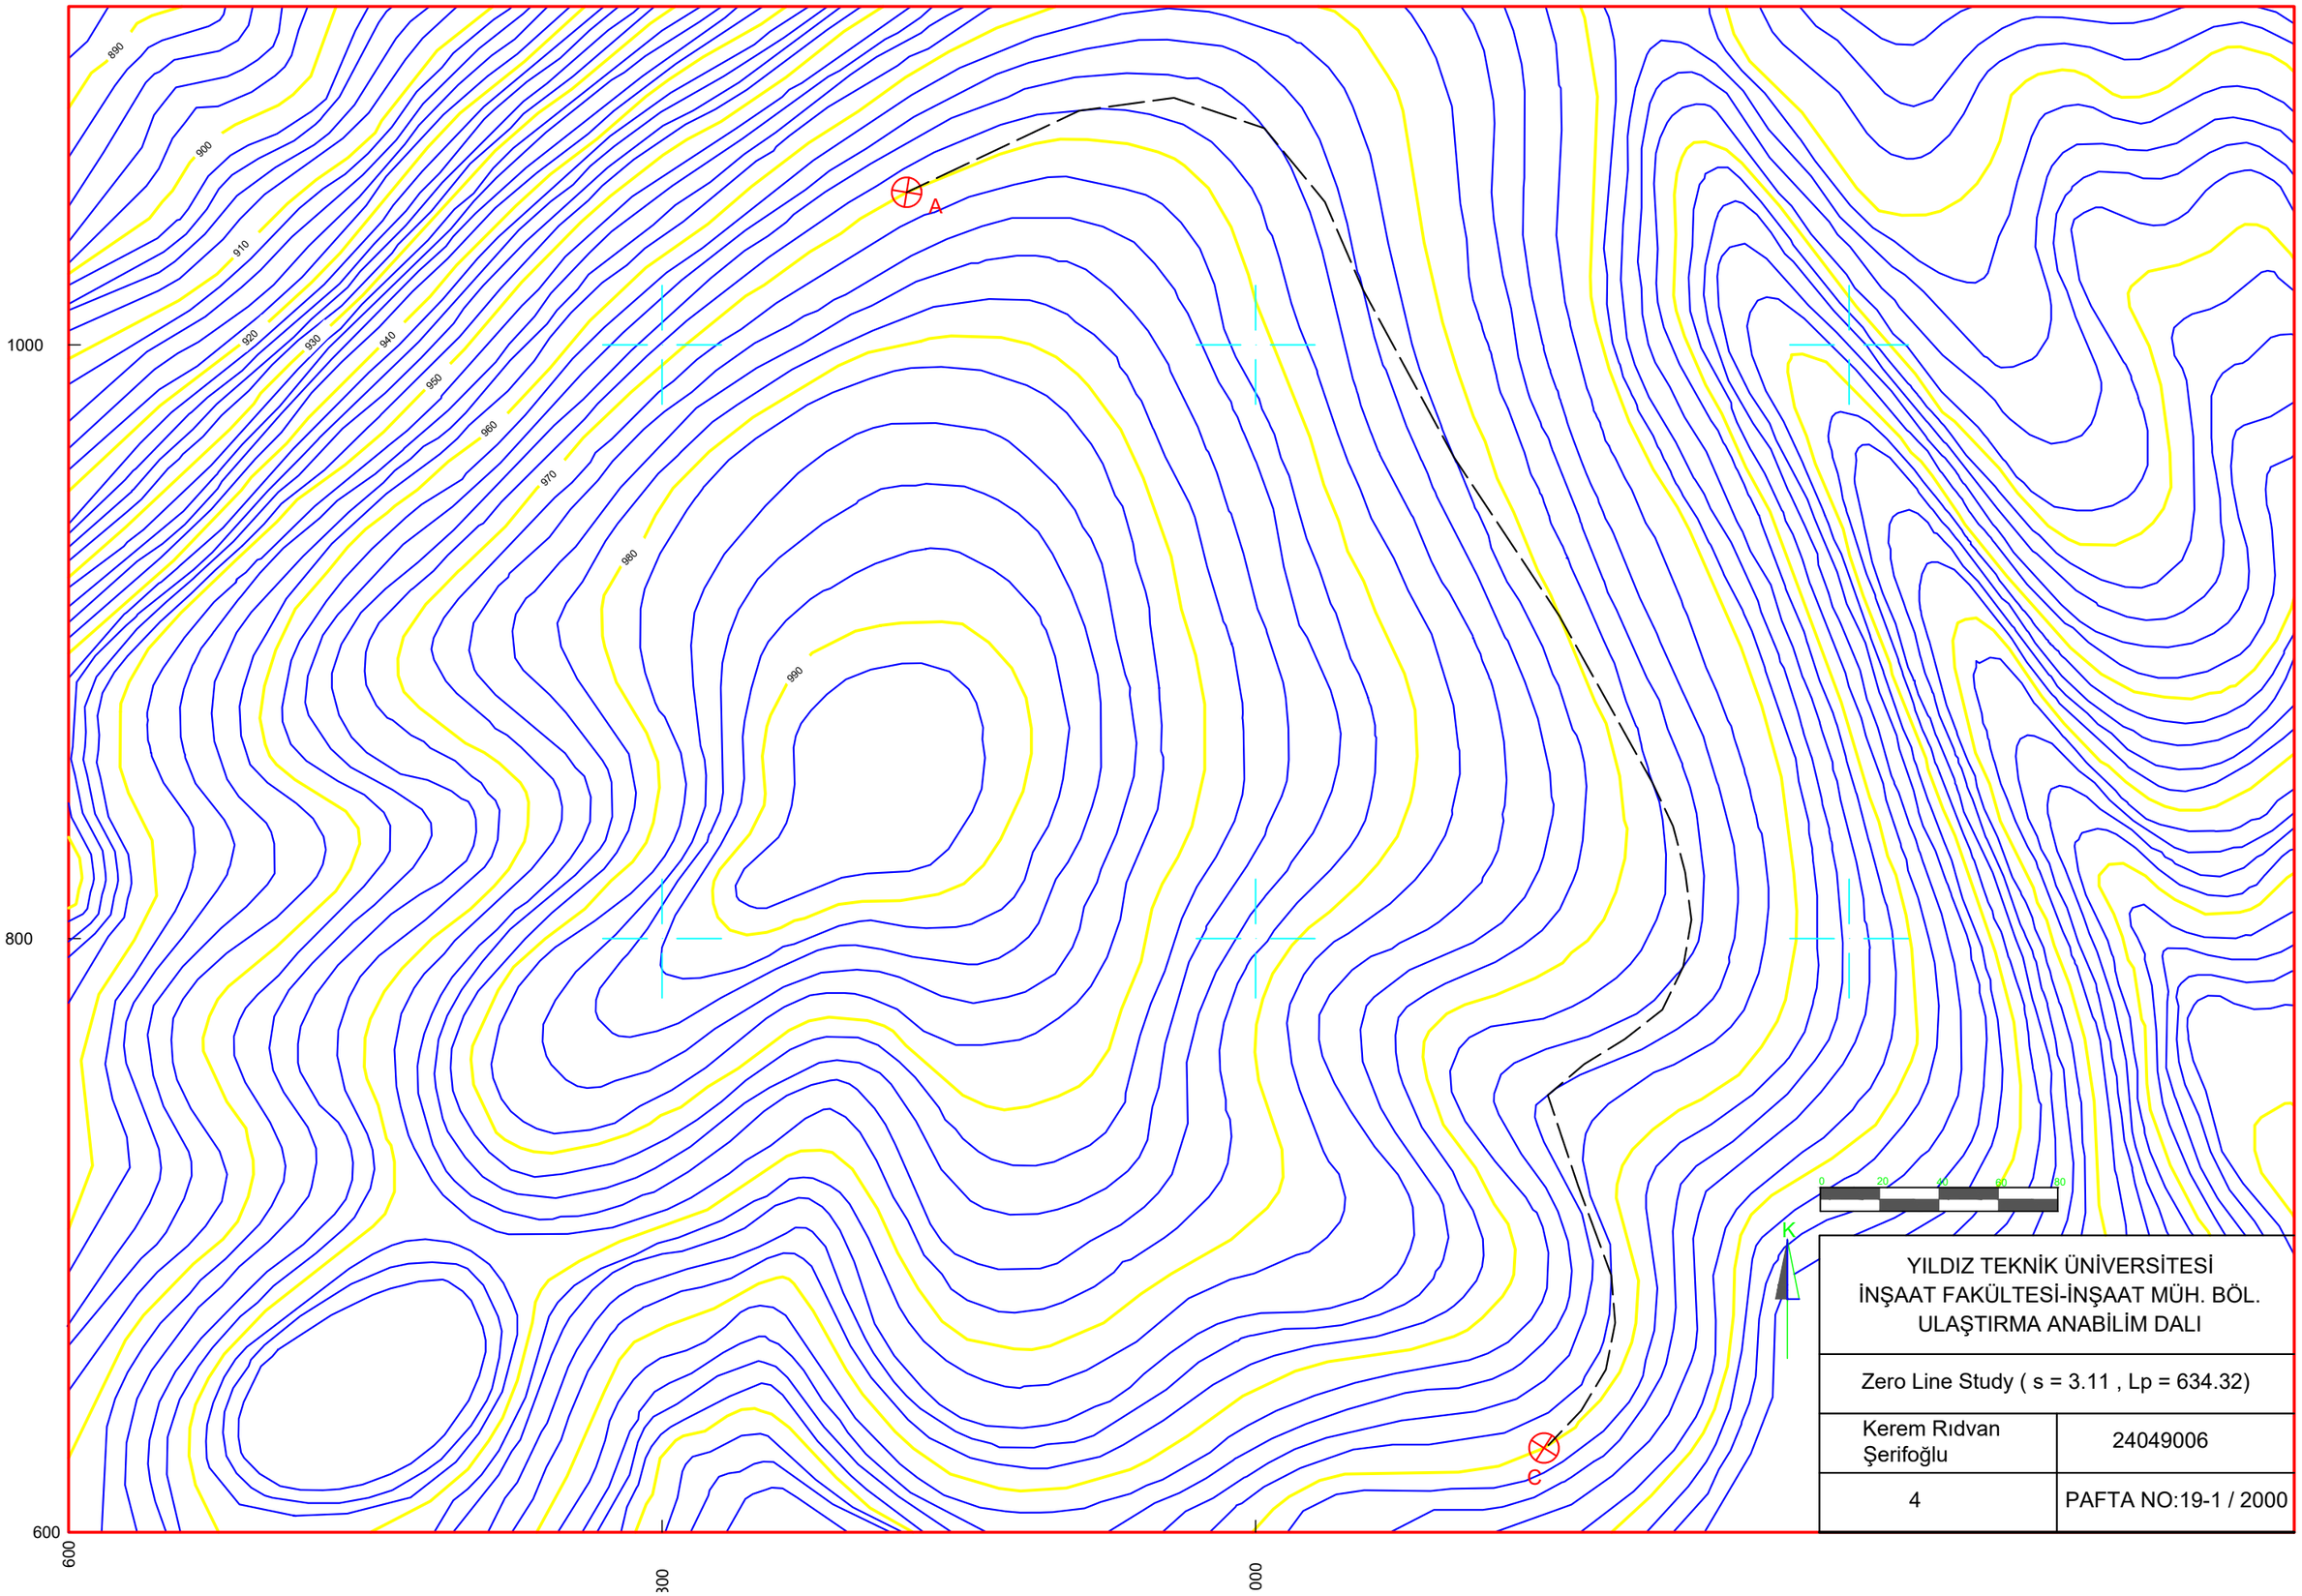


YILDIZ TEKNİK ÜNİVERSİTESİ İNŞAAT FAKÜLTESİ-İNŞAAT MÜH. BÖL. ULAŞTIRMA ANABİLİM DALI	
Zero Line Study (s = 3.11 , Lp = 634.32)	
Kerem Rıdvan Şerifoğlu	24049006
4	PAFTA NO:19-1 / 2000